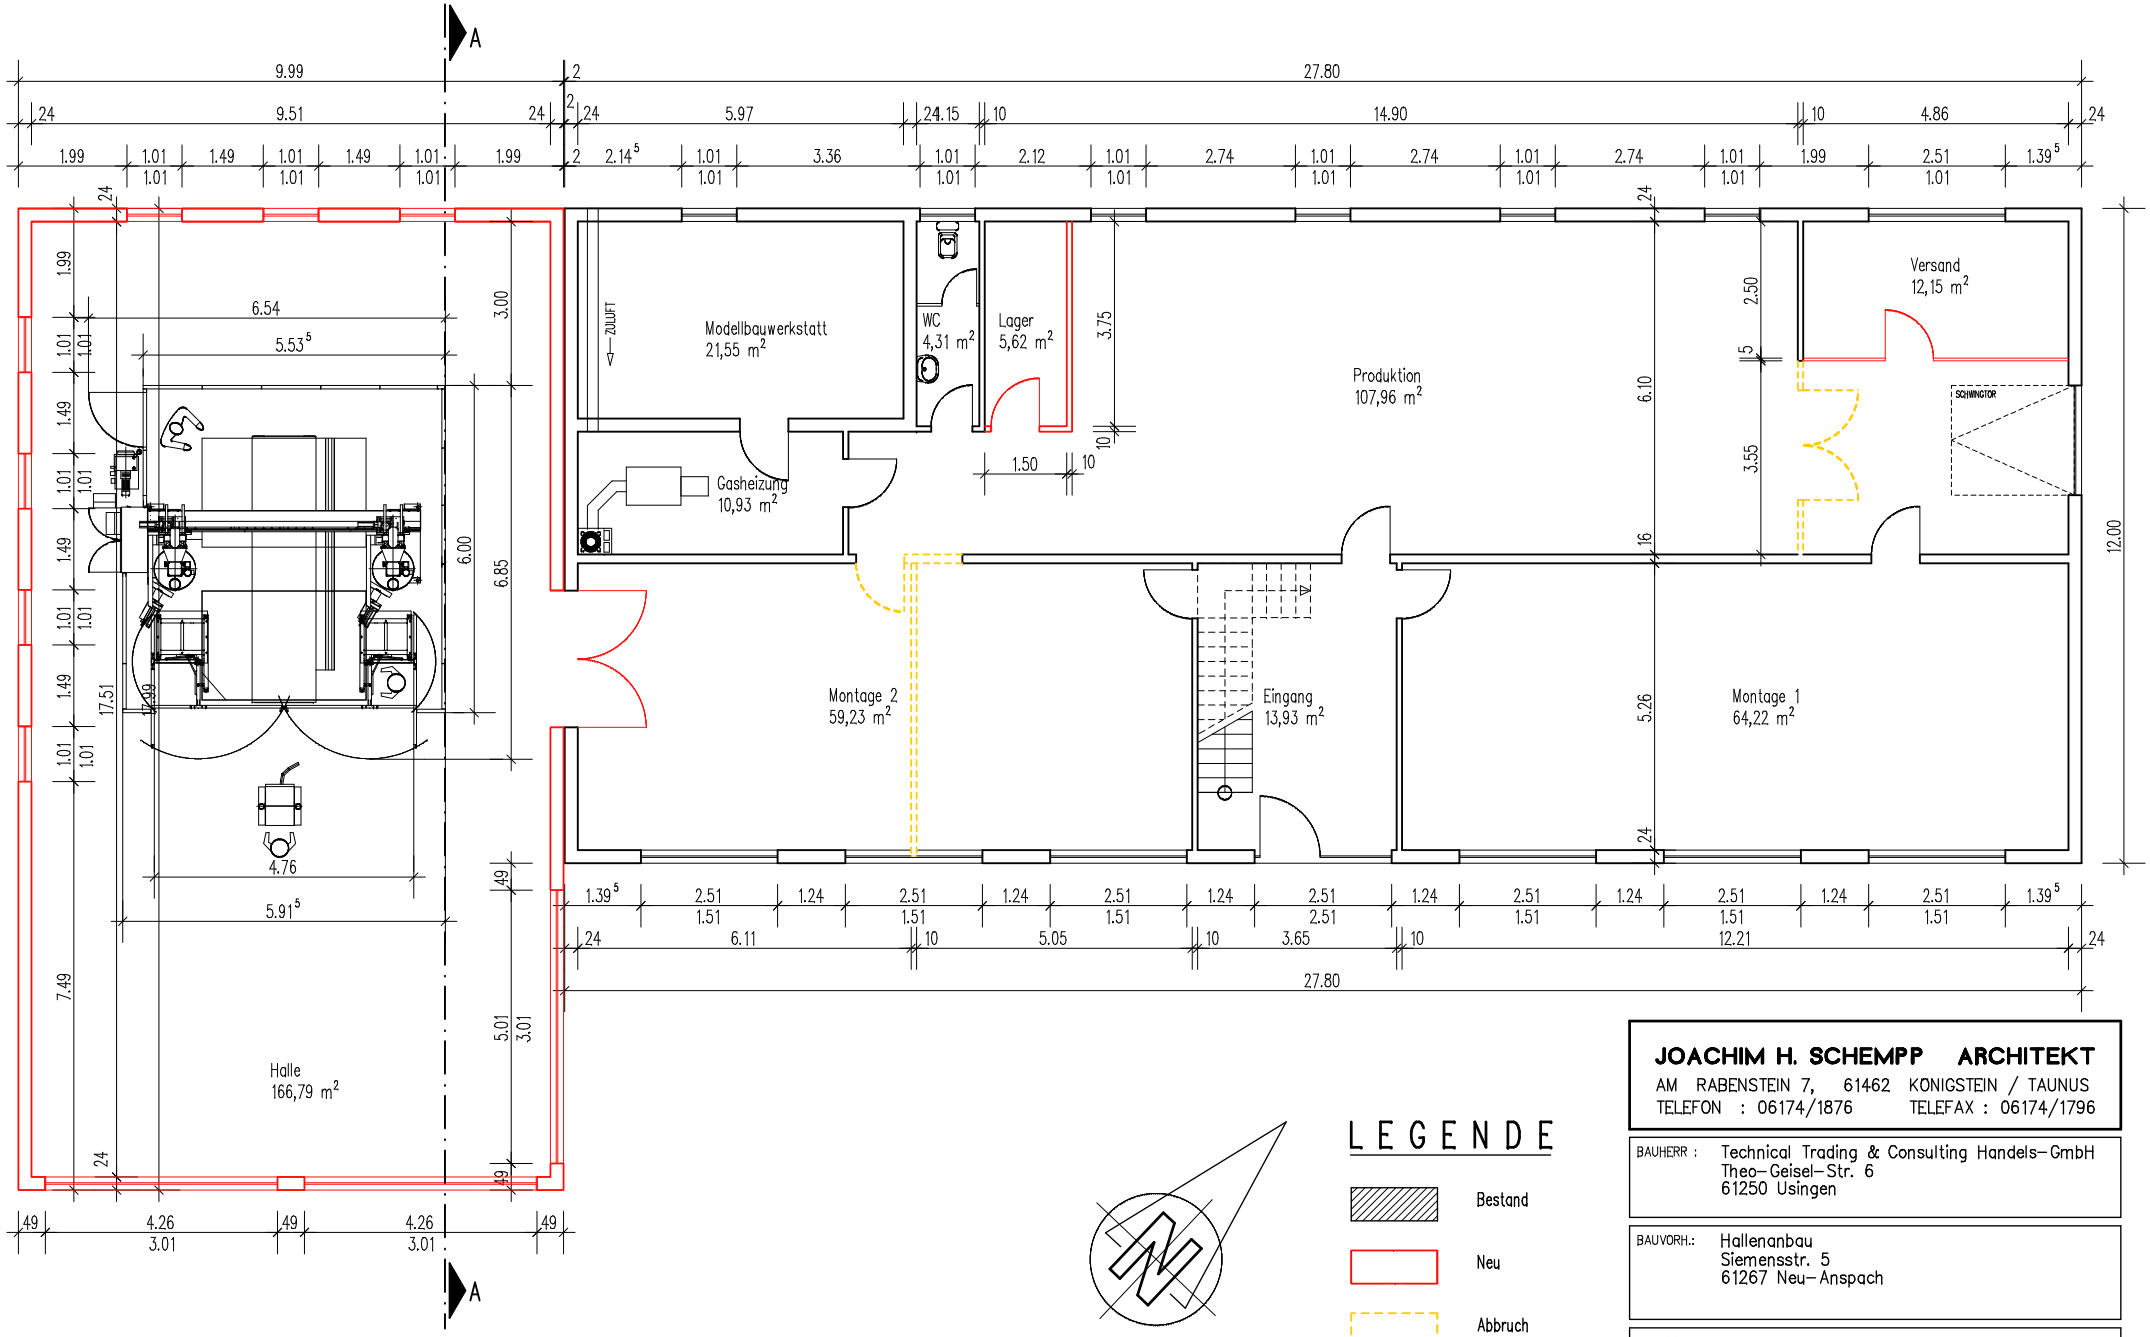

LEGENDE

- Bestand
- Neu
- Abbruch

JOACHIM H. SCHEMPP ARCHITEKT
AM RABENSTEIN 7, 61462 KONIGSTEIN / TAUNUS
TELEFON : 06174/1876 TELEFAX : 06174/1796

BAUHERR : Technical Trading & Consulting Handels-GmbH
Theo-Geisel-Str. 6
61250 Usingen

BAUVORH.: Hallenanbau
Siemensstr. 5
61267 Neu-Anspach

PLANBEZ.: **Erdgeschoss**

GEZ.:	DATUM :	PLAN-NR.:	PLOT-DAT.:	
REI	27.04.09	3322/01	27.04.09	M 1:100

TTC100 | Plan: E | Plot: TTC100_E

ANDERUNG : | DATUM: